



STAKING PLOT
STRUCTURES

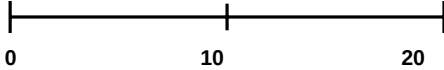

GRAPHIC SCALE: 1" = 10'

4 points

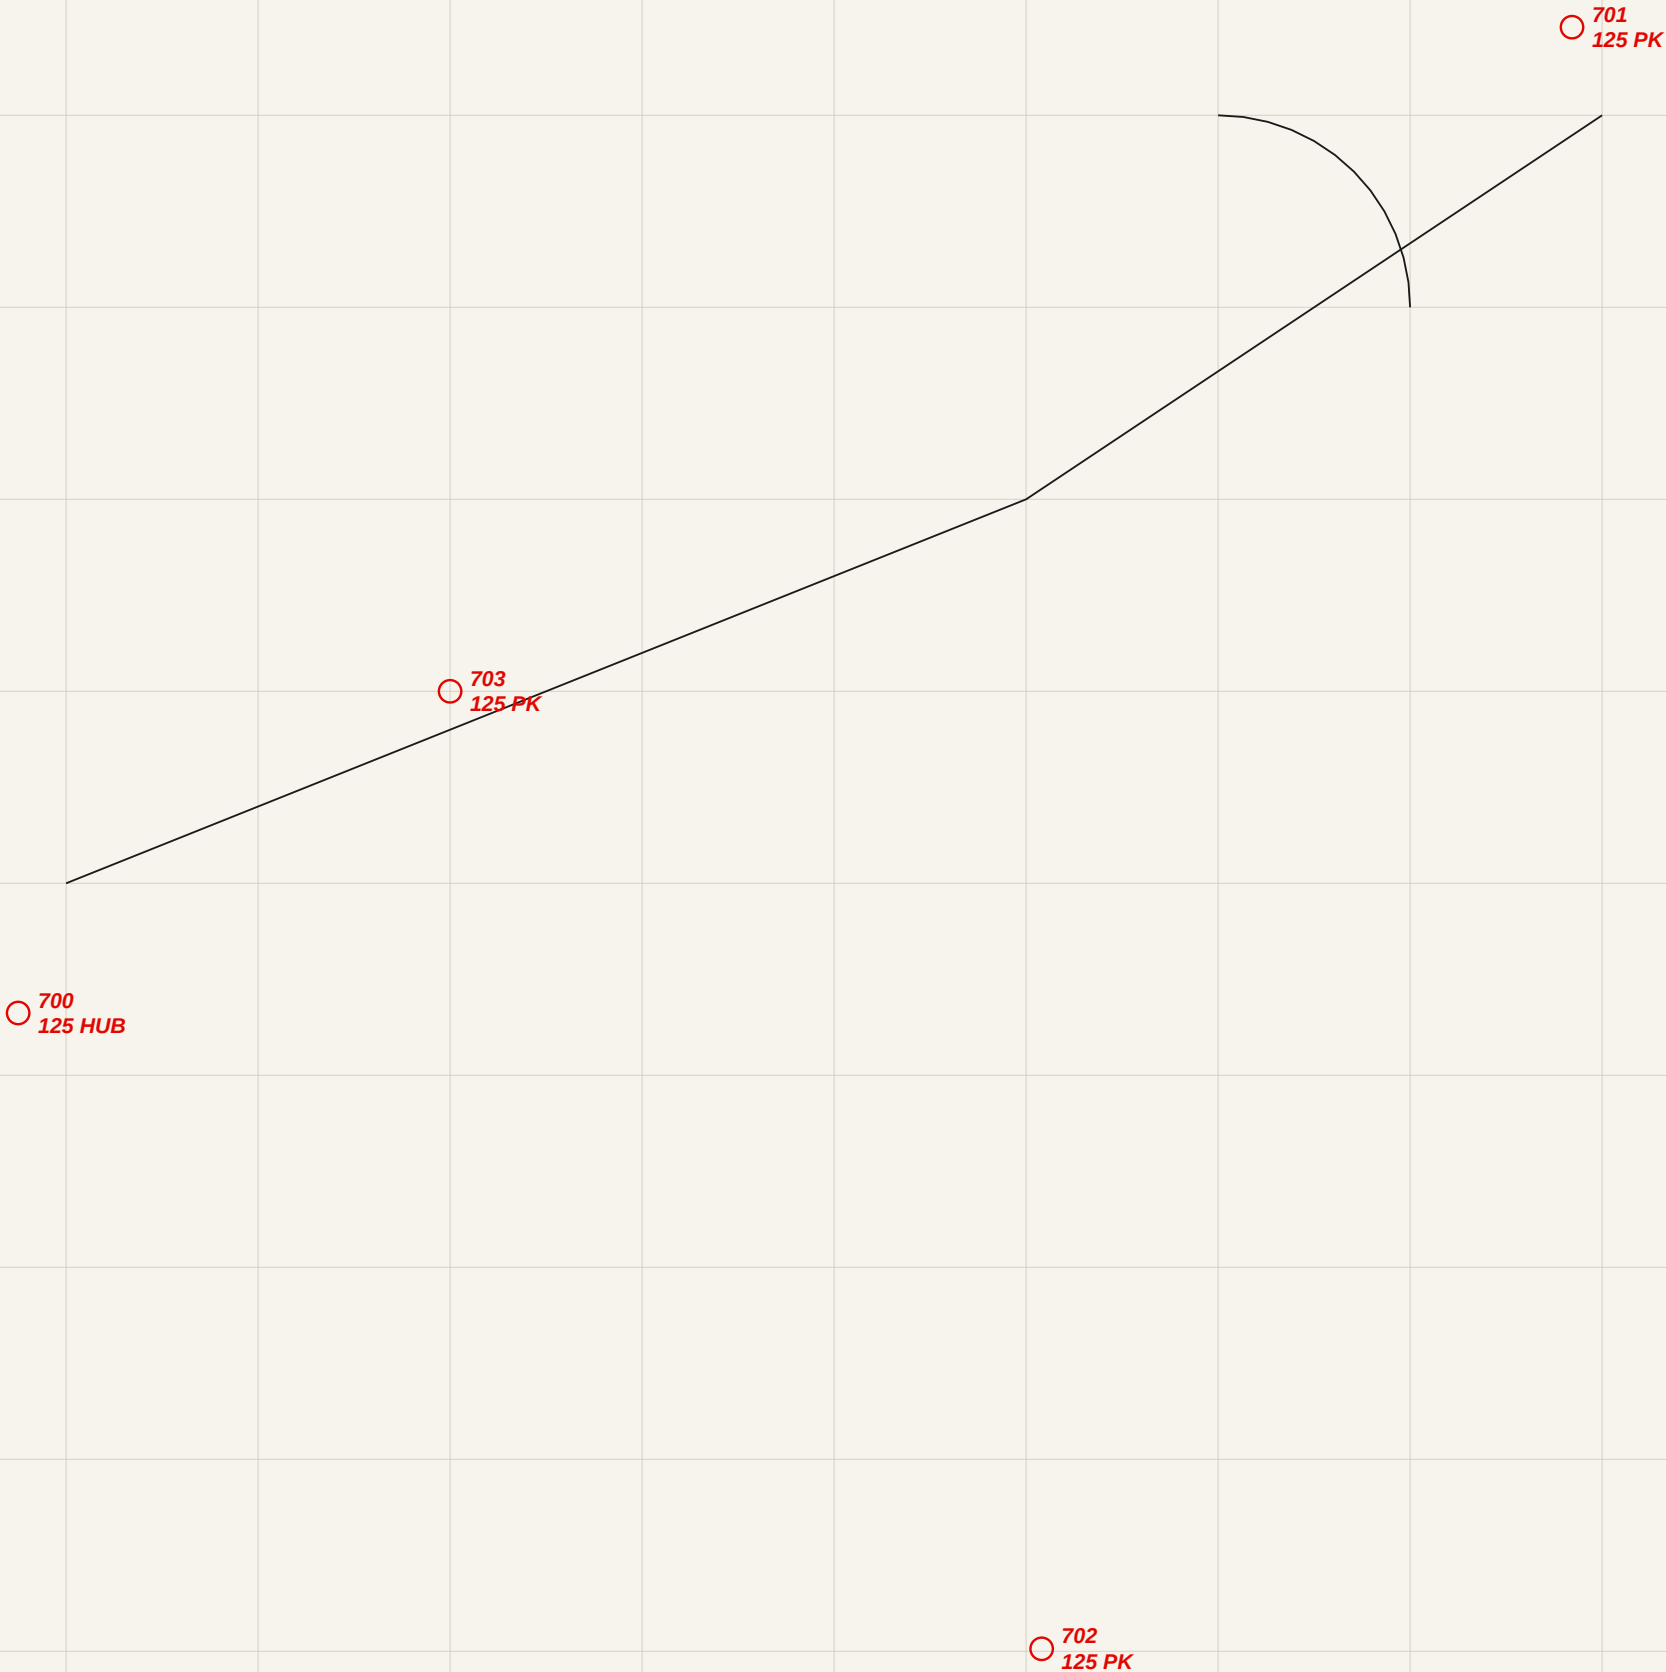

NOTE: Points shown were established for construction staking. It is the responsibility of the end user to verify points and use good survey practices before relying on this plot in the field.

TRIO Engineering, LLC
4100 N. Calhoun Rd., Suite 300
Brookfield, WI 53005
262.790.1480