


# STAKING PLOT


## CONTROL CHECK

| CONTROL POINTS |             |           |            |             |
|----------------|-------------|-----------|------------|-------------|
| Point #        | Description | Elevation | Northing   | Easting     |
| 700            | 125 HUB     | 961.66    | 410233.245 | 2495897.503 |
| 701            | 125 PK      | 958.51    | 410284.590 | 2495978.433 |
| 702            | 125 PK      | 964.80    | 410200.130 | 2495950.810 |
| 703            | 125 PK      | 970.58    | 410250.000 | 2495920.000 |

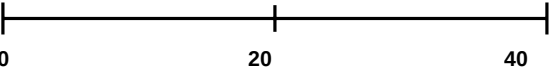

GRAPHIC SCALE: 1" = 20'

4 points

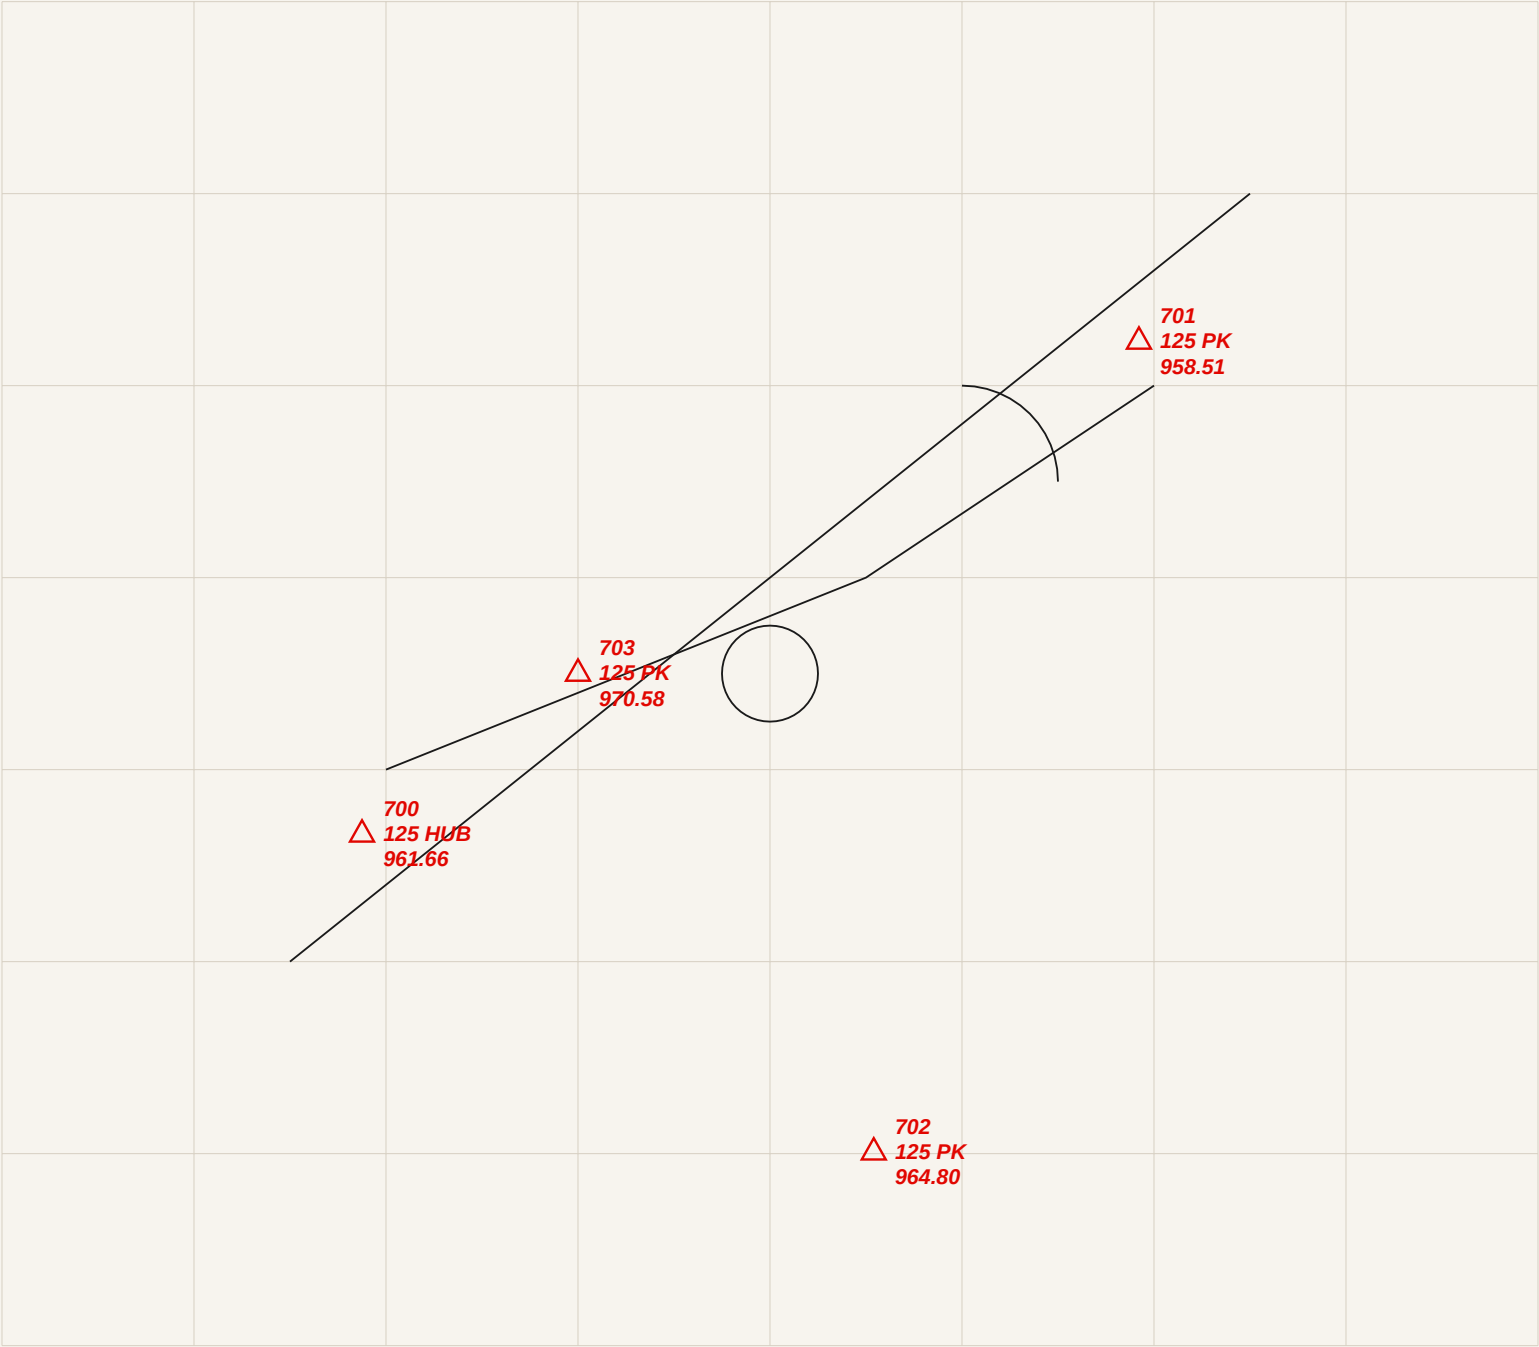

NOTE: Points shown were established for construction staking. It is the responsibility of the end user to verify points and use good survey practices before relying on this plot in the field.

TRIO Engineering, LLC  
4100 N. Calhoun Rd., Suite 300  
Brookfield, WI 53005  
262.790.1480

DATE: 07/24/26  
PAGE 1 OF 1