



STAKING PLOT

WILDFLOWER

CONTROL POINTS				
Point #	Description	Elevation	Northing	Easting
700	125 HUB	961.66	410233.245	2495897.503
701	125 PK	958.51	410284.590	2495978.433
702	125 PK	964.80	410200.130	2495950.810
703	125 PK	970.58	410250.000	2495920.000
704	IP	962.10	410215.500	2495910.200
705	CURB	959.40	410265.800	2495945.600
706	CATCH	960.05	410240.100	2495965.000
707	BOC	966.20	410275.200	2495905.400
708	EOC	963.55	410222.700	2495935.800
709	MH	957.90	410255.300	2495988.100

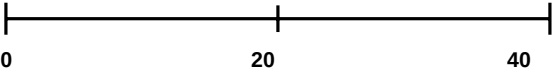

GRAPHIC SCALE: 1" = 20'
10 points

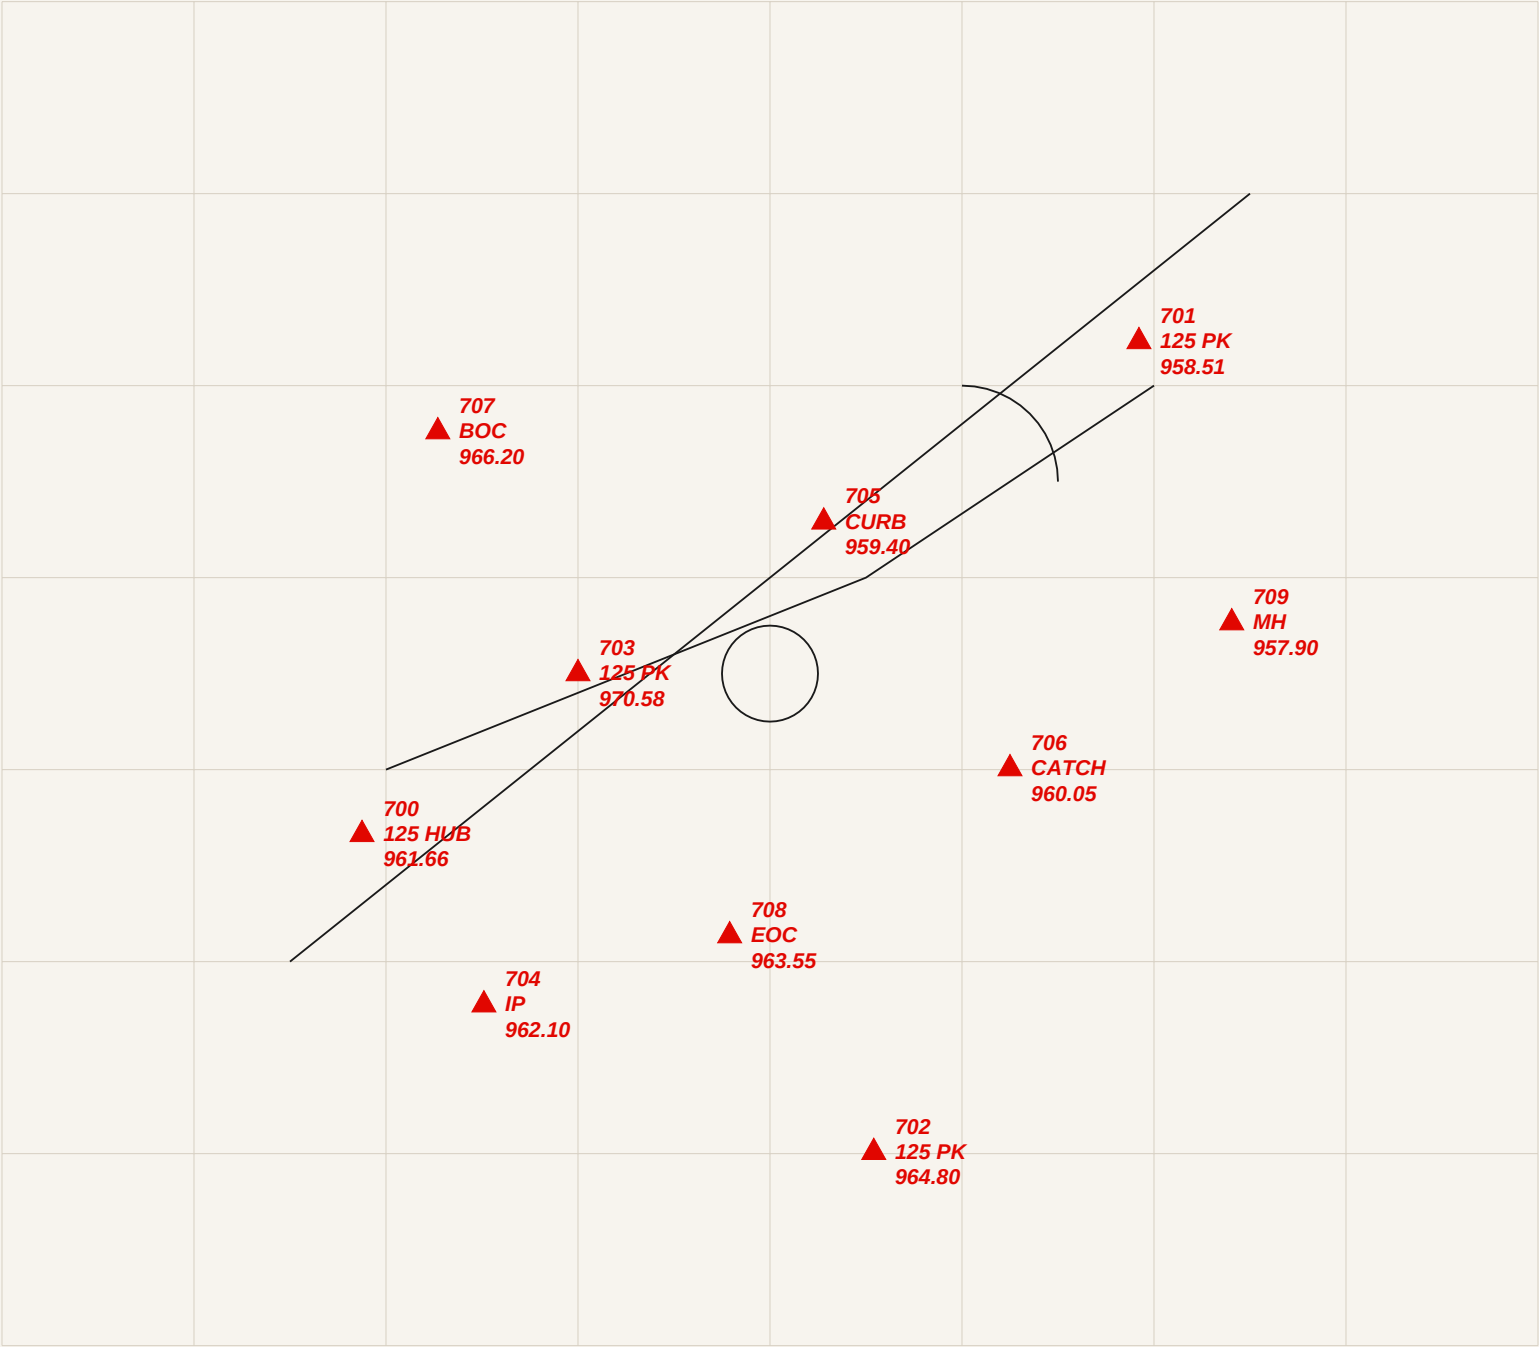

NOTE: Points shown were established for construction staking. It is the responsibility of the end user to verify points and use good survey practices before relying on this plot in the field.

TRIO Engineering, LLC
4100 N. Calhoun Rd., Suite 300
Brookfield, WI 53005
262.790.1480

DATE: 07/24/26
PAGE 1 OF 1