



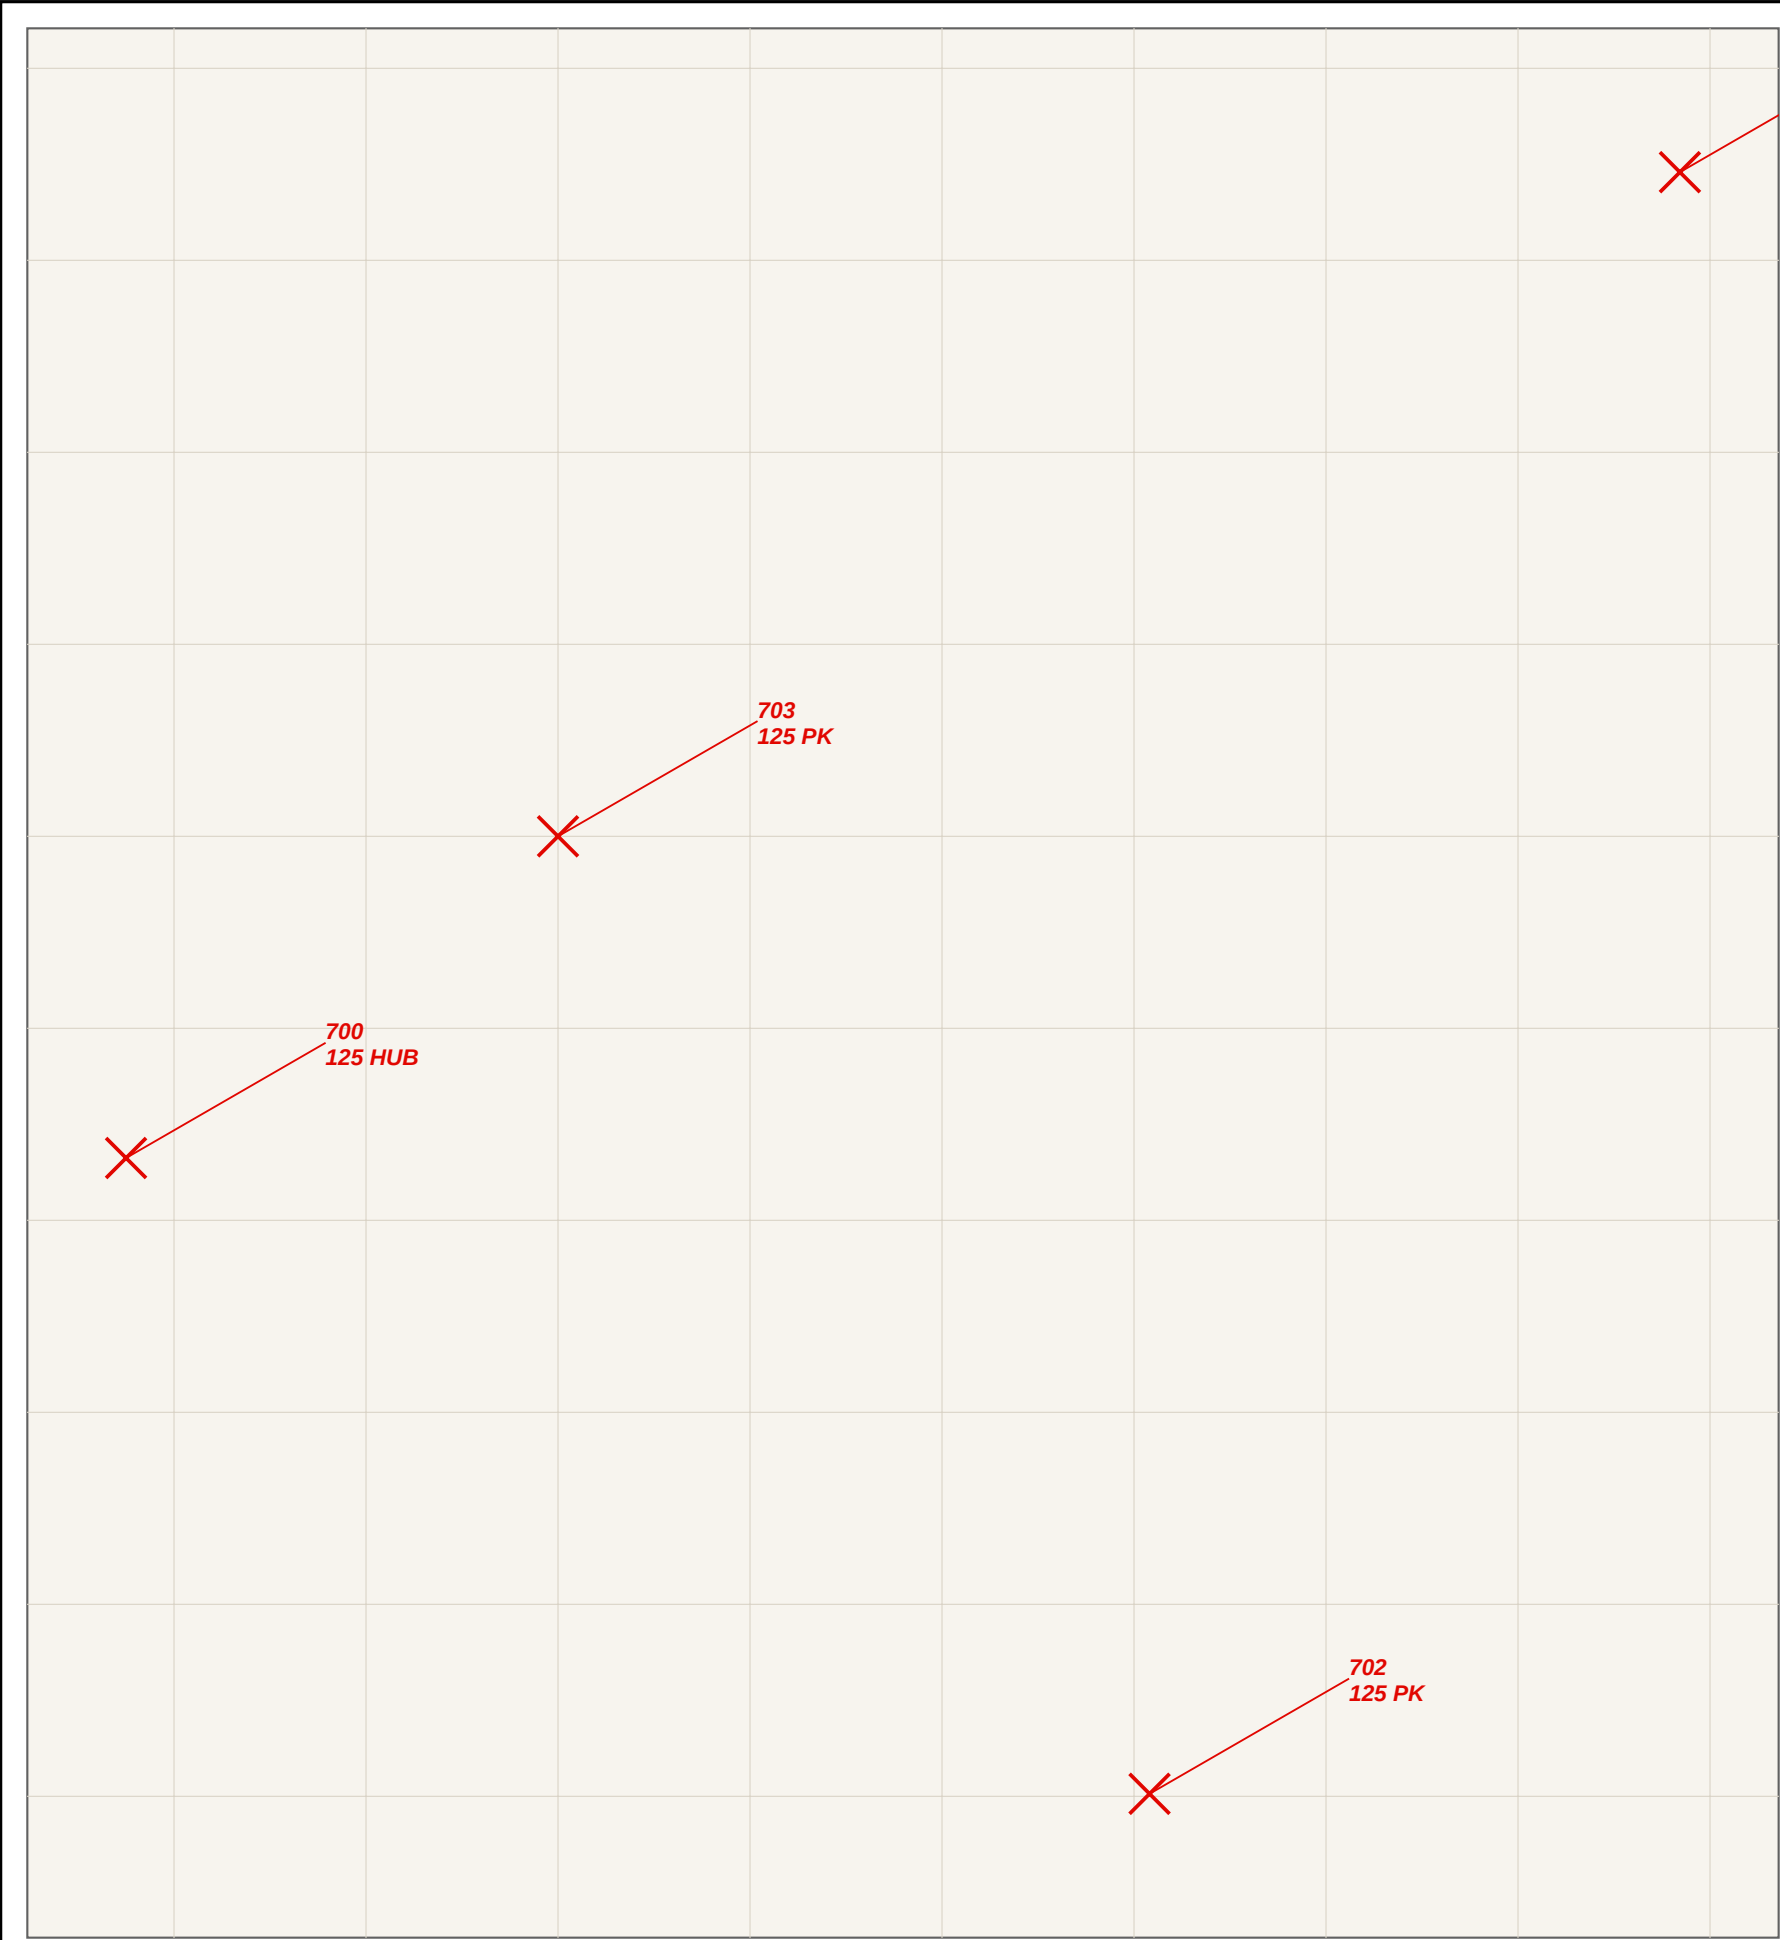

STAKING PLOT

ALPINE HILLS

CONTROL POINTS				
Point #	Description	Elevation	Northing	Easting
700	125 HUB	961.66	410233.245	2495897.503
701	125 PK	958.51	410284.590	2495978.433
702	125 PK	964.80	410200.130	2495950.810
703	125 PK	970.58	410250.000	2495920.000

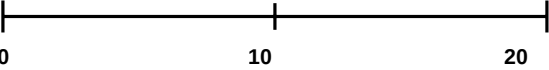

GRAPHIC SCALE: 1" = 10'
(17"×11")

4 points

NOTE: Points shown were established for construction staking. It is the responsibility of the end user to verify points and use good survey practices before relying on this plot in the field.

TRIO Engineering, LLC
4100 N. Calhoun Rd., Suite 300
Brookfield, WI 53005
262.790.1480

DATE: 07/15/26
PAGE 1 OF 1