


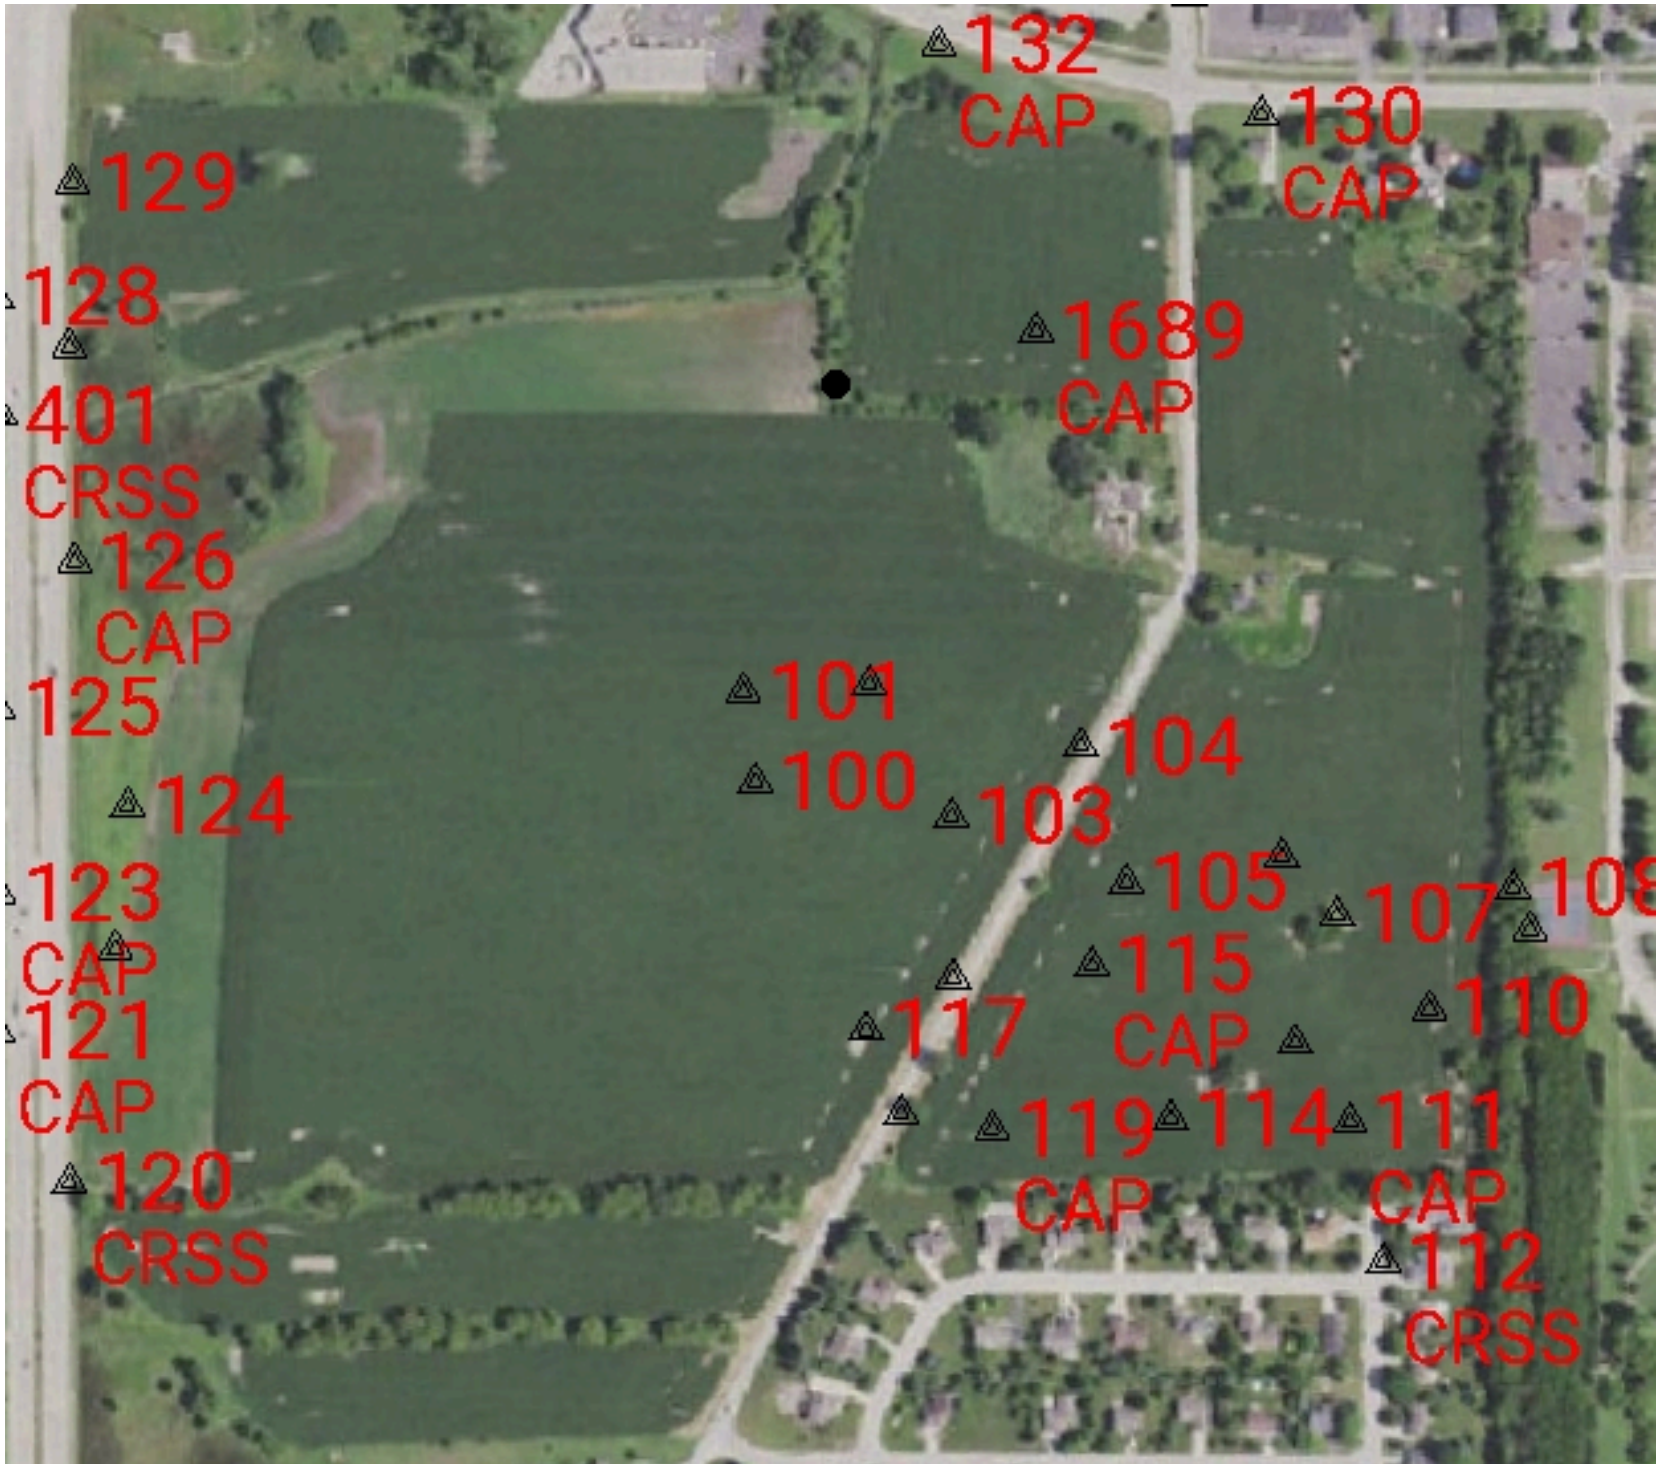


CONTROL POINTS				
Point #	Description	Elevation	Northing	Easting
81	CHIS T	946.56	416277.119	2468791.731
85	CHIS T	942.23	418329.788	2470690.958
100	CAP	949.11	417007.695	2470031.257
101	CAP	947.10	417171.766	2470009.811
102	CAP	952.54	417184.318	2470237.341
103	CAP	951.47	416944.677	2470385.939
104	CAP	956.26	417072.188	2470619.537
105	CAP	953.23	416825.776	2470701.658
107	CAP	951.70	416767.030	2471082.513
108	CRSS	950.50	416815.498	2471400.776
109	CRSS	948.05	416741.338	2471431.333
110	CAP	948.05	416598.030	2471249.580
111	CAP	949.03	416393.819	2471106.013
112	CRSS	950.48	416141.048	2471166.847
113	CAP	949.79	416536.752	2471006.525
114	CAP	950.52	416400.265	2470782.070
115	CAP	954.08	416676.332	2470639.821
116	CAP	954.44	416654.809	2470388.564
117	CAP	954.04	416560.155	2470231.513
118	CAP	953.34	416409.051	2470295.335
119	CAP	953.27	416381.942	2470459.291
120	CRSS	946.64	416284.860	2468791.994
121	CAP	946.25	416556.772	2468661.725
122	CAP	941.68	416707.322	2468874.904
123	CAP	947.32	416807.500	2468663.344
124	CAP	941.57	416964.131	2468897.175
125	CAP	947.08	417141.336	2468662.430
126	CAP	943.97	417406.490	2468800.834
127	CAP	943.73	417794.054	2468790.925
128	CAP	944.76	417882.915	2468659.137
129	CAP	943.05	418089.233	2468797.234
130	CAP	945.17	418211.831	2470946.108
131	CRSS	944.65	418427.369	2470814.793
132	CAP	941.13	418338.713	2470362.381
133	RBR	952.88	416872.966	2470982.460
401	CRSS	945.73	417670.039	2468667.423
402	NWFLGBLT	956.86	417110.416	2470308.538
403	NW FLG BLT	953.07	416746.576	2471240.569
404	NW FLG BLT	951.04	416514.792	2471130.305
405	NW FLG BLT	953.88	416495.956	2470553.258
BASE01	POLE	954.44	416737.173	2471416.606

NOTE:
THESE CONTROL POINTS WERE ESTABLISHED BY TRIO ENGINEERING, LLC USING GPS EQUIPMENT.

IT IS THE RESPONSIBILITY OF THE END USER OF SAID POINTS TO USE GOOD SURVEY PRACTICES TO VERIFY THE POINTS HAVE NOT CHANGED SINCE BEING SET.

THE END USER OF THIS INFORMATION SHALL NOTIFY TRIO ENGINEERING, LLC OF ANY DISCREPANCIES NOTICED BETWEEN PROVIDED CONTROL POINTS. TRIO ENGINEERING, LLC WILL NOT BE HELD LIABLE FOR OTHERS USE OF SAID CONTROL POINTS.

CONTROL NOTE WILDFLOWER-STARK

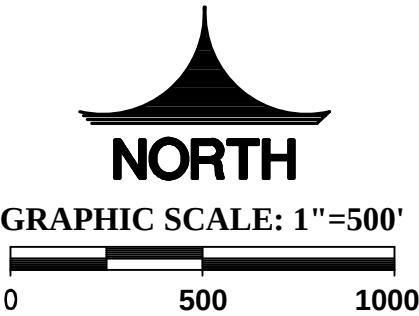

4100 N. Calhoun R.
Suite 300
Brookfield, WI 53005
Phone: (262) 790-1480
Fax: (262) 790-1481