



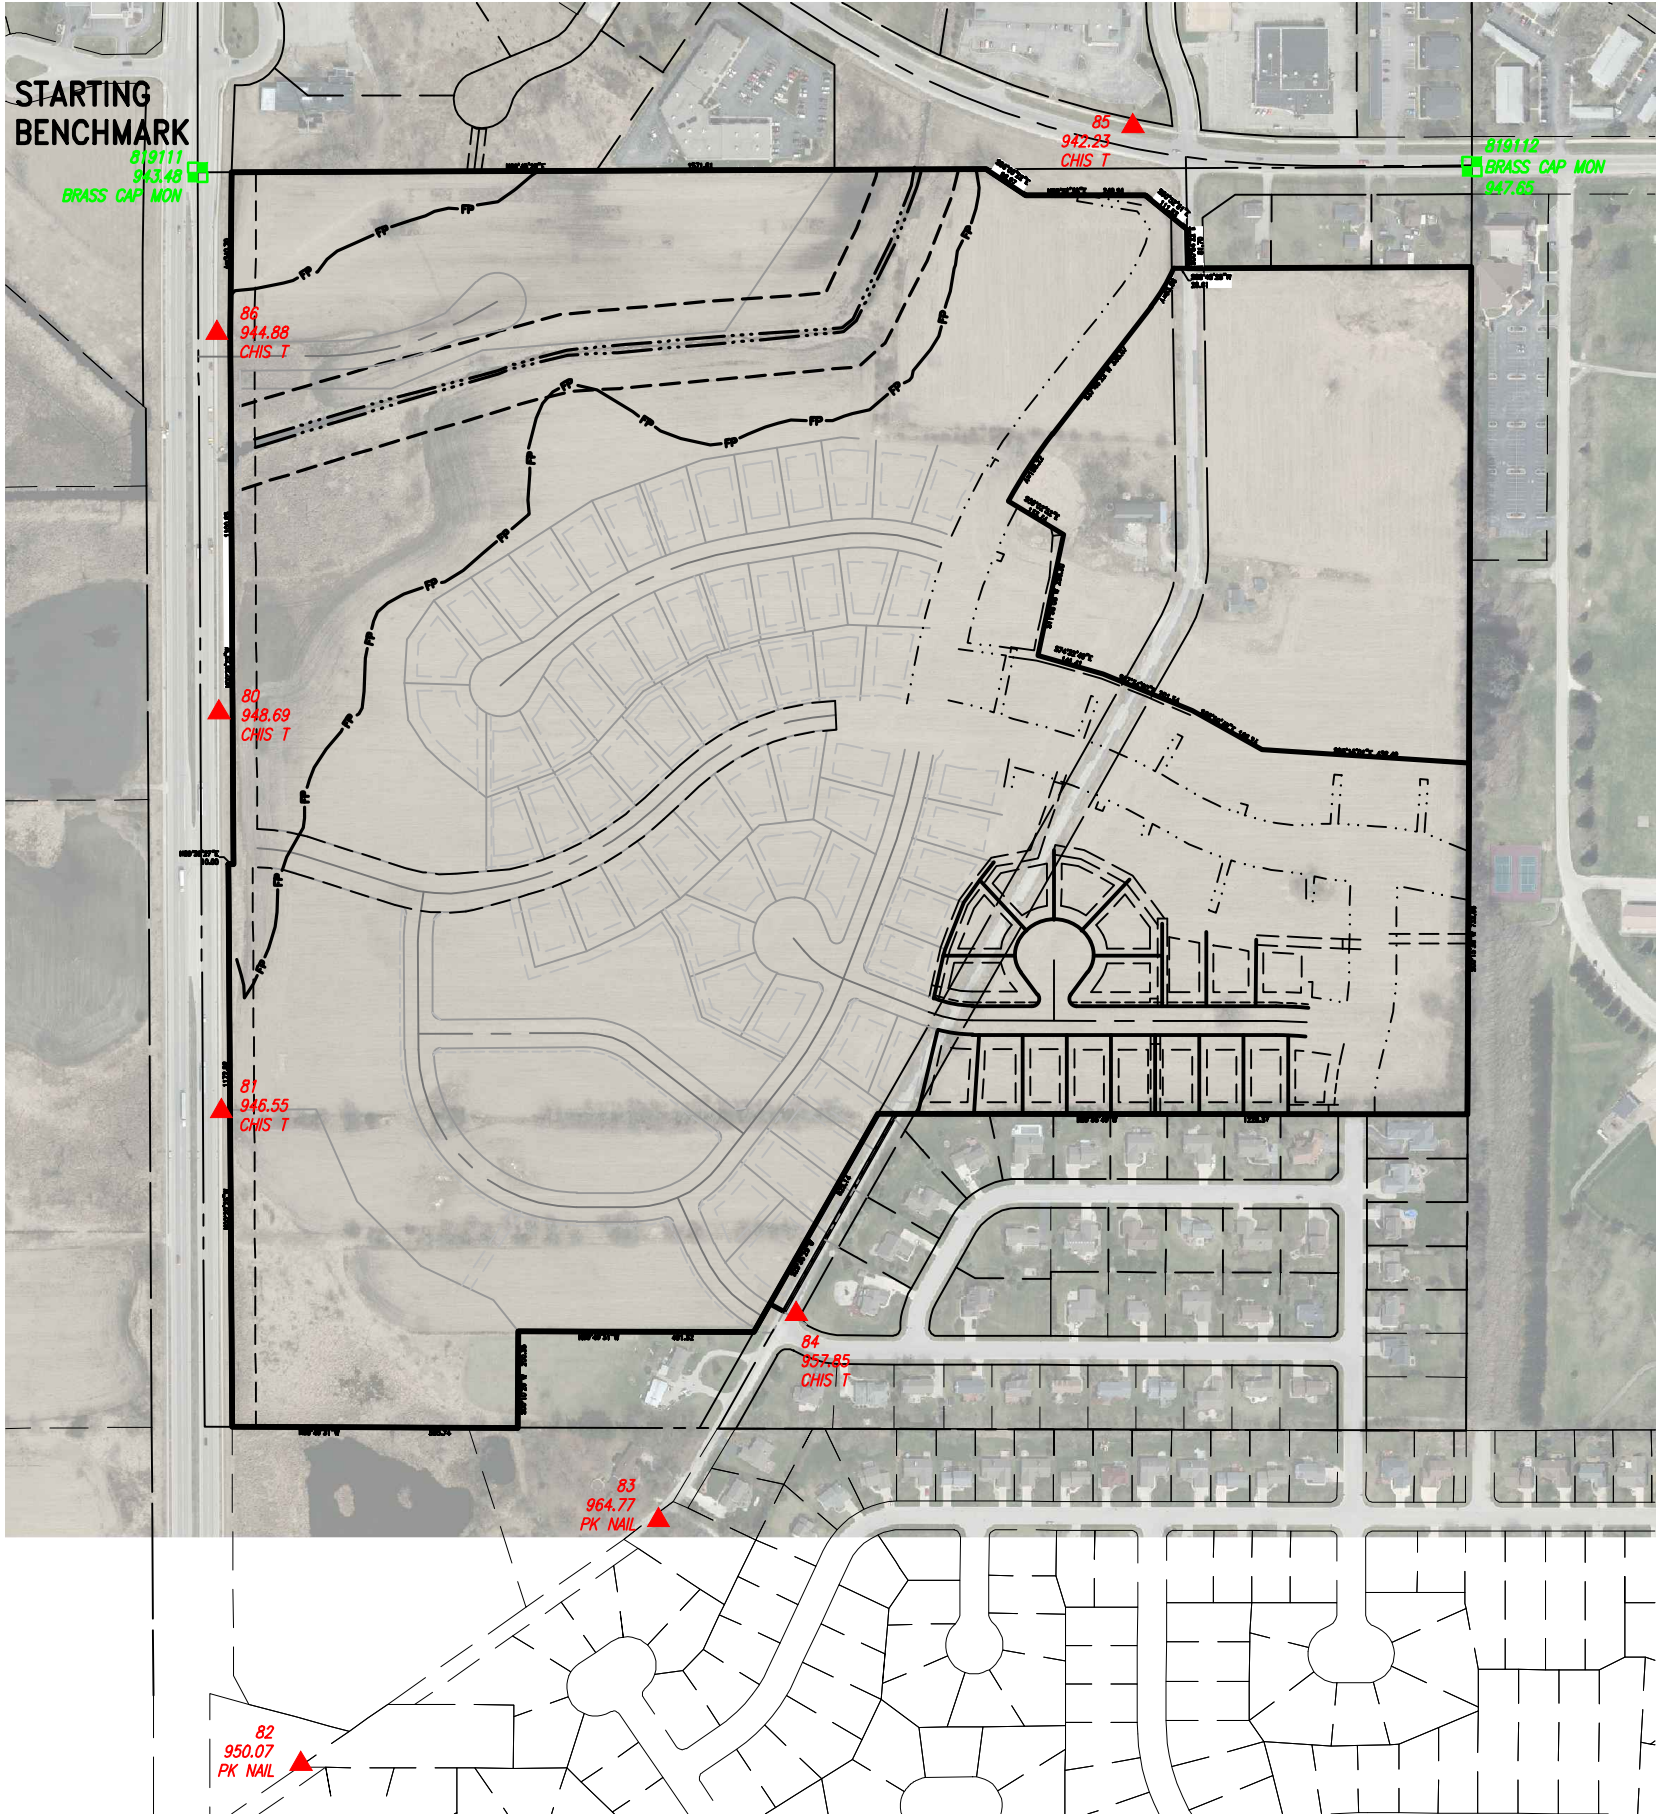

CONTROL POINTS				
Point #	Description	Elevation	Northing	Easting
80	125 CHIS T	948.69	417108.082	2468786.790
81	125 CHIS T	946.55	416277.134	2468791.716
82	125 PK NAIL	950.07	414916.627	2468957.828
83	125 PK NAIL	964.77	415424.479	2469702.787
84	125 CHIS T	957.85	415853.807	2469989.830
85	125 CHIS T	942.23	418329.796	2470690.994
86	125 CHIS T	944.88	417898.603	2468782.355

CONTROL NOTE ALPINE HILLS

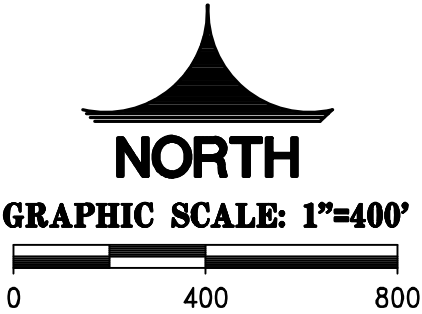

NOTE:
THESE CONTROL POINTS WERE ESTABLISHED
BY TRIO ENGINEERING, LLC USING GPS
EQUIPMENT.

IT IS THE RESPONSIBILITY OF THE END
USER OF SAID POINTS TO USE GOOD
SURVEY PRACTICES TO VERIFY THE POINTS
HAVE NOT CHANGED SINCE BEING SET.

THE END USER OF THIS INFORMATION SHALL
NOTIFY TRIO ENGINEERING, LLC OF ANY
DISCREPANCIES NOTICED BETWEEN PROVIDED
CONTROL POINTS. TRIO ENGINEERING, LLC
WILL NOT BE HELD LIABLE FOR OTHERS USE
OF SAID CONTROL POINTS.



4100 N. Calhoun R.
Suite 300
Brookfield, WI 53005
Phone: (262) 790-1480
Fax: (262) 790-1481